Согласовано

Инв. N подл. | Подп. и дата | Взам. инв. N

Изм.	Кол. уч.	Лист	N док.	Подп.	Дата
Разраб.		Смирнова			06.24
Провер.		Елисеев			06.24
Н.контр.		Филатов			06.24

«Многоквартирные 2-х, 3-х, 4-х этажные жилые дома со встроенными нежилыми помещениями 5 этап строительства: поз. 5.1, 5.2, 5.3, 5.4, 5.5, расположенные по адресу: Белгородская область, г. Старый Оскол, Микрорайон Центральный на территории ограниченной улицами Островского, Ленина, 33 Богатырей, Ленина»

Конструкции типового этажа.

Стадия	Лист	Листов
Р	1	

ПК "ПРОЕКТ"

Формат А2

Согласовано

Инв. N подл. | Подп. и дата | Взам. инв. N

Изм.	Кол.уч.	Лист	N док.	Подп.	Дата
Разраб.		Смирнова			06.24
Провер.		Елисеев			06.24
Н.контр.		Филатов			06.24

«Многоквартирные жилые дома с встроенными нежилыми помещениями 5 этап строительства: поз. 5.1, 5.2, 5.3, 5.4, 5.5, расположенные по адресу: Белгородская область, г. Старый Оскол, Микрорайон Центральный на территории ограниченной ул. Островского, Ленина и ул. 31 Конструкции типового этажа.

Стадия	Лист	Листов
Р	2	

ПК "ПРОЕКТ"

Формат А2

Согласовано

Инв. N подл. | Подп. и дата | Взам. инв. N

Изм.	Кол. уч.	Лист	N док.	Подп.	Дата
Разраб.		Смирнова			06.24
Провер.		Елисеев			06.24
Н.контр.		Филатов			06.24


«Многоквартирные жилые дома с встроенными нежилыми помещениями 5 этап строительства: поз. 5.1, 5.2, 5.3, 5.4, 5.5, расположенные по адресу: Белгородская область, г. Старый Оскол, Микрорайон Центральный на территории ограниченной ул. Островского, Ленина и ул. Конституции СССР»

Конструкции типового этажа.

Стадия	Лист	Листов
Р	3	

ПК "ПРОЕКТ"

Формат А2

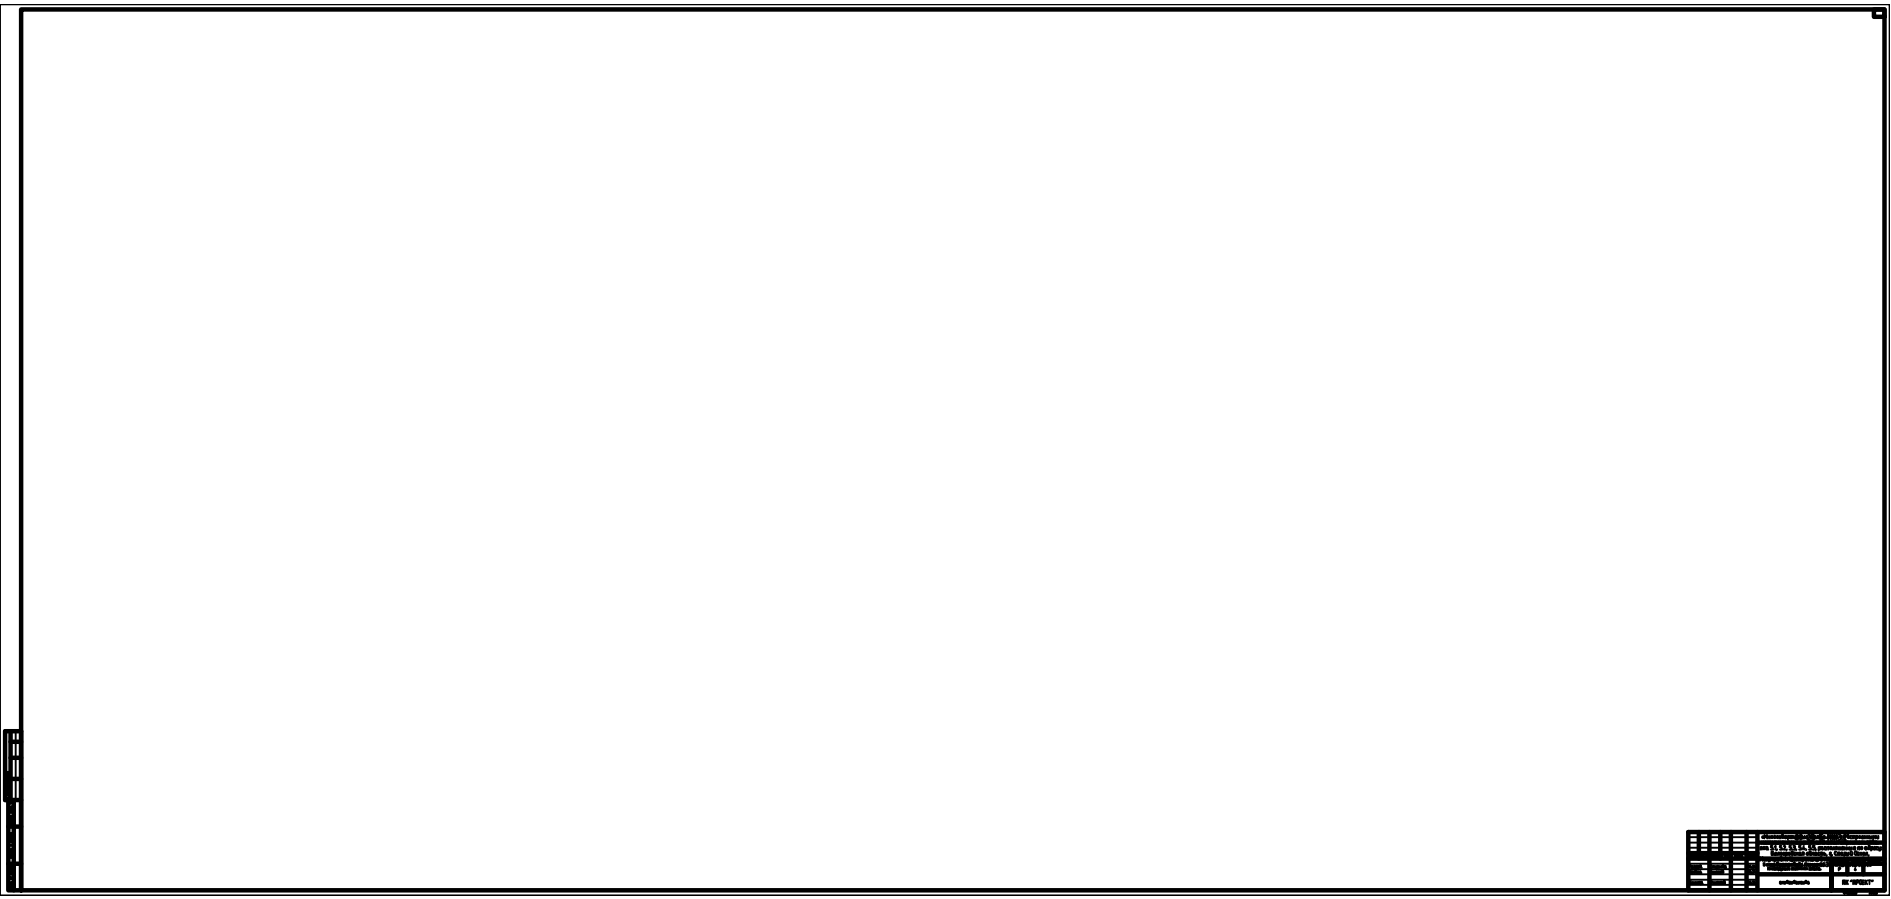

Согласовано

Взам. инв. №

Подп. и дата

Инв. № подл.

Изм.	Кол. уч.	Лист	№ док.	Подп.	Дата
Разраб.		Смирнова			06.24
Провер.		Елисеев			06.24
Н.контр.		Филатов			06.24

«Многоквартирные жилые дома со встроенными нежилыми помещениями. 5 этап строительства: поз. 5.1, 5.2, 5.3, 5.4, 5.5, расположенные по адресу: Белгородская область, г. Старый Оскол, Микрорайон Центральный на земельном участке с кадастровым номером 31:06:0206012:4264»

5 этап строительства. Позиция 5.3. Конструкции типового этажа.

Стадия	Лист	Листов
Р	5	

амыбаыбаыаыва

ПК "ПРОЕКТ"

Формат А3